




Abwicklung 1:25

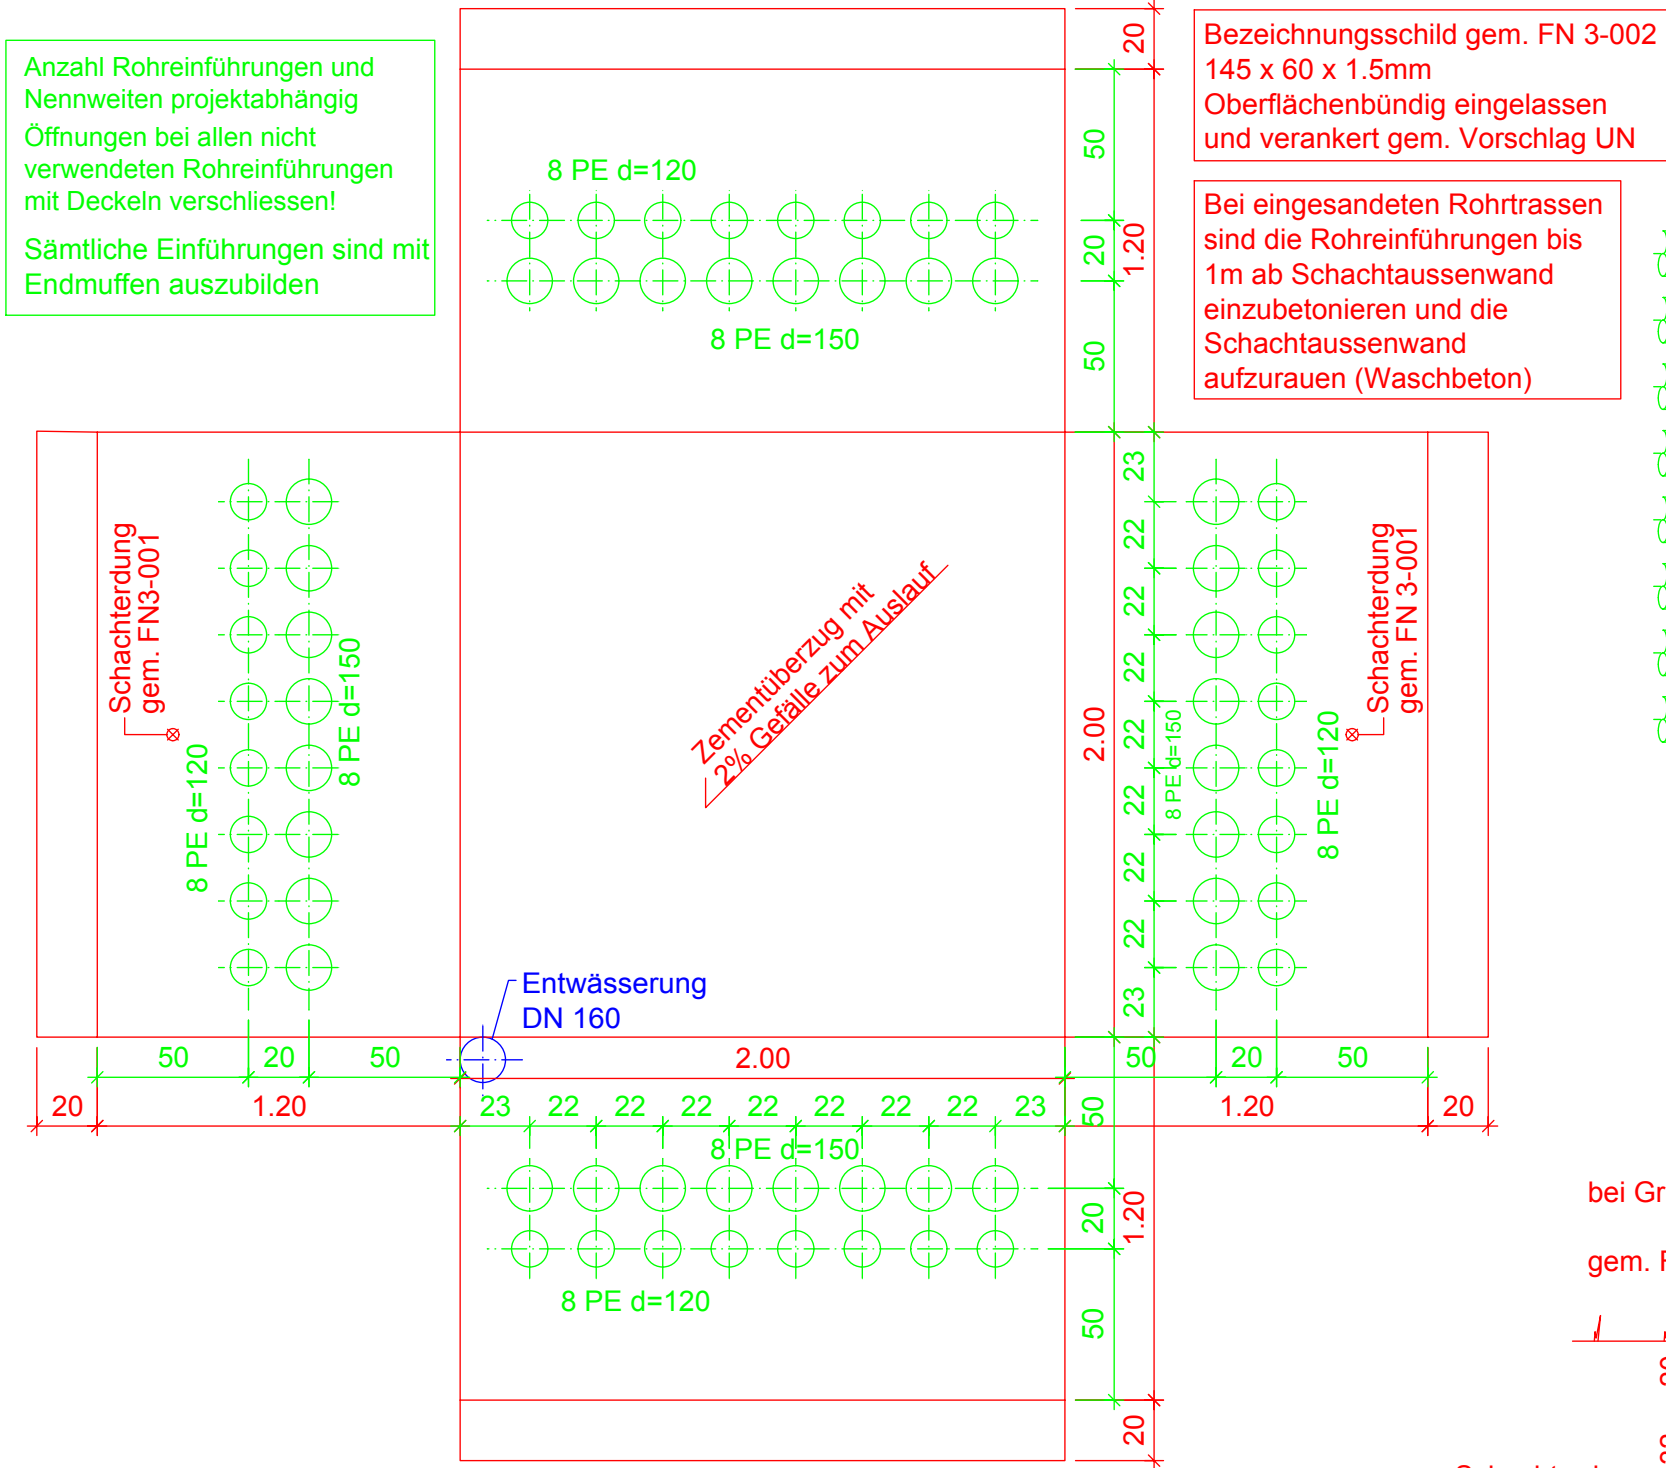

Grundriss 1:25

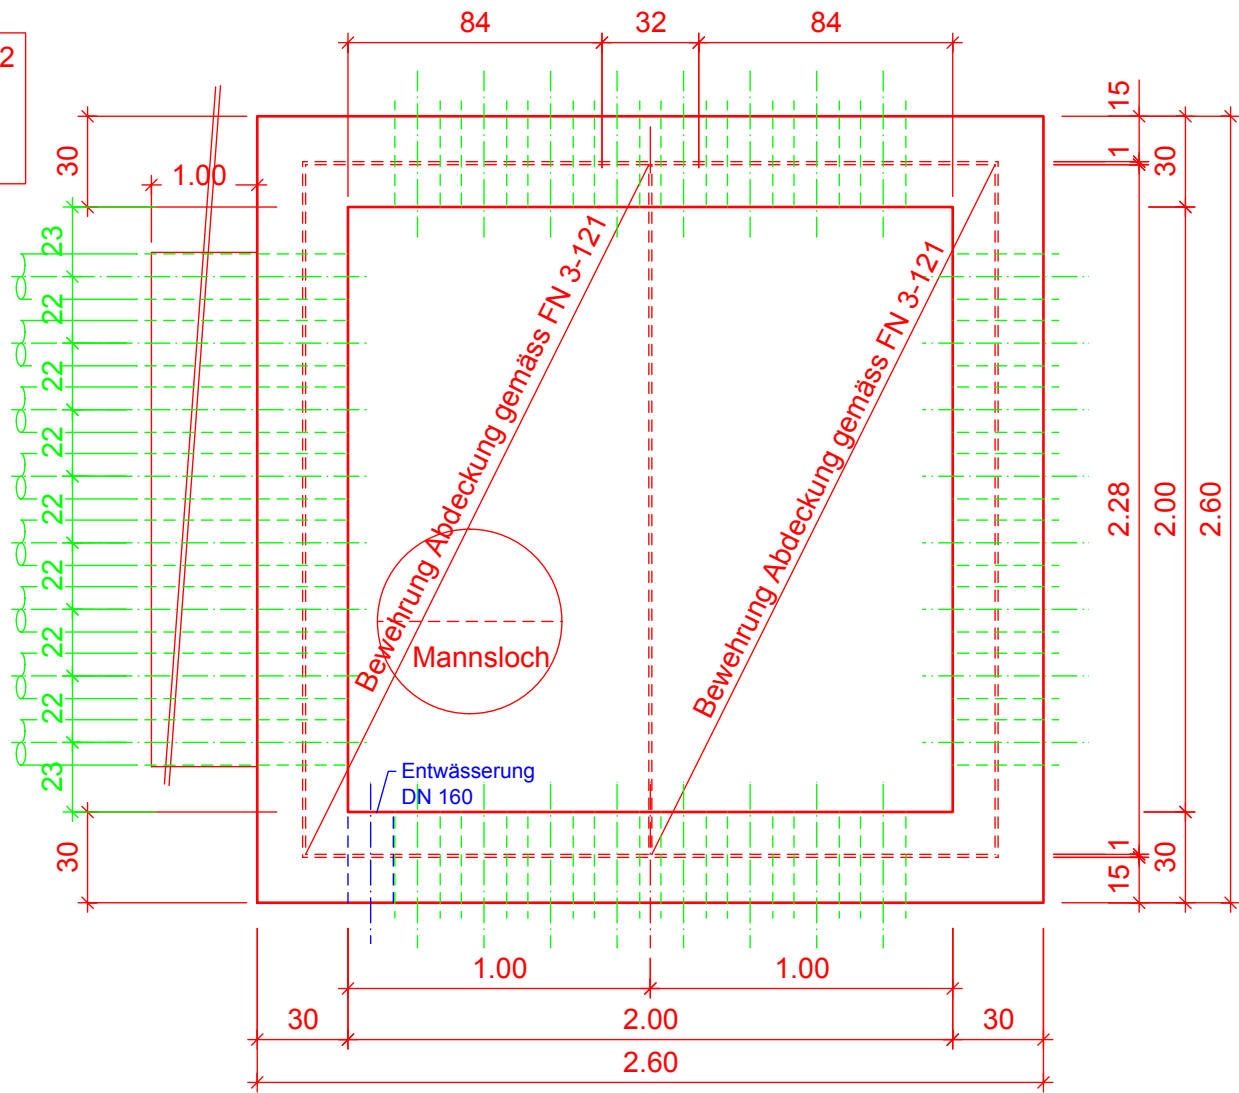

Querschnitt 1:25

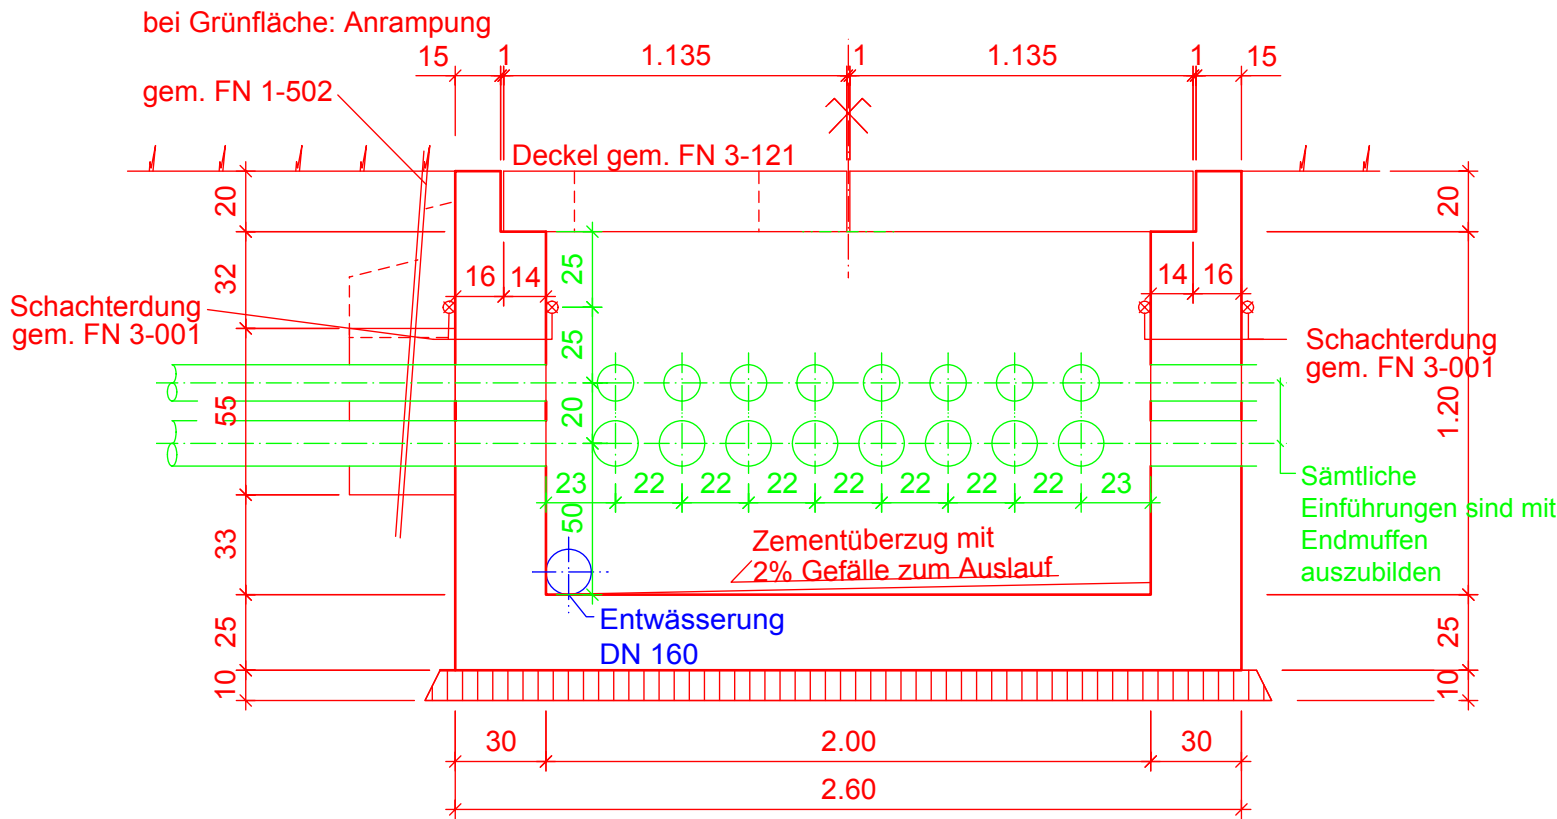

Beton: C30/37, XC4(CH), XF1(CH), Dmax = 32mm, CI 0.1 (NPK C gem. SN EN 206-1)

NORMALIEN	FLUGHAFENZÜRICH	FN	3-120
Elektroanlagen		Rev.	Datum
Kabelschacht Typ IV		-	09.12.2015
Anwendungsbereich D		a	31.05.2018
Schalung			
Dazugehörige FN: 3-121			